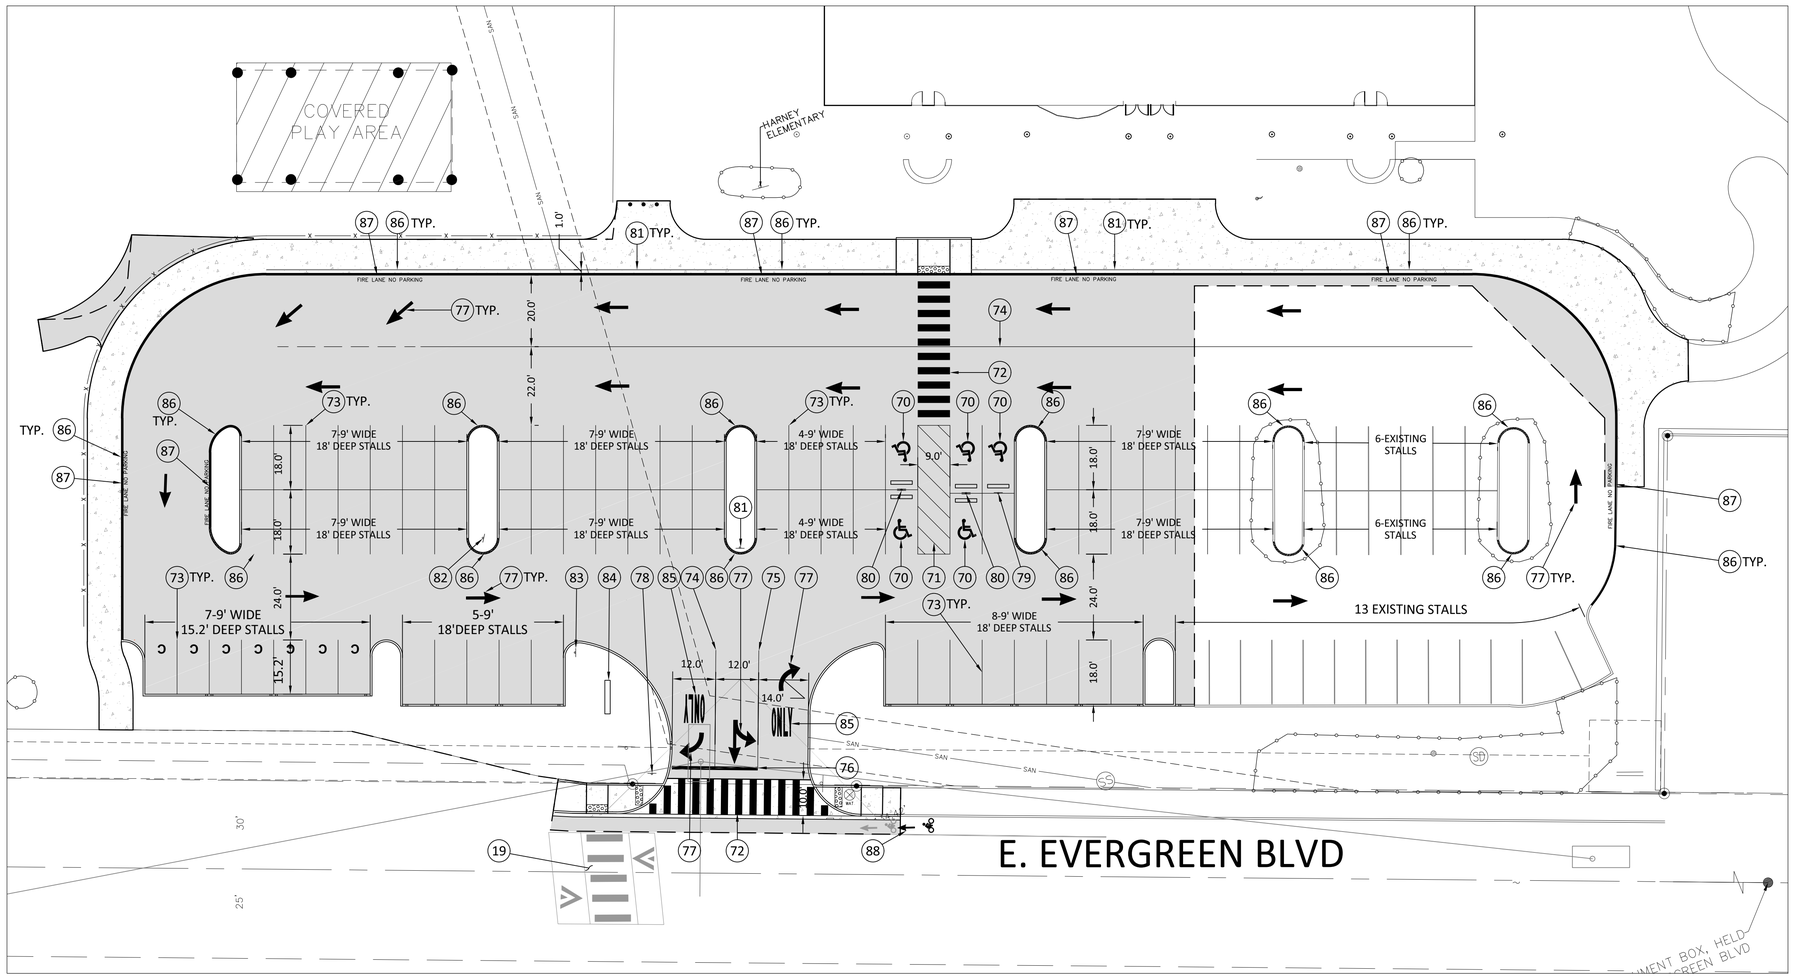

PLAN VIEW
SCALE: 1" = 20'

SCALE: 1" = 20'

CITY OF VANCOUVER

THESE PLANS HAVE BEEN REVIEWED FOR COMPLIANCE WITH CITY CODES, ORDINANCES AND POLICIES AND ARE

APPROVED

THE APPROVAL OF THESE PLANS BY THE CITY OF VANCOUVER DOES NOT AUTHORIZE ANY NONCOMPLIANCE WITH LOCAL ORDINANCE, CODE OR STATE LAW.

THESE PLANS SHALL BE AVAILABLE FOR ALL REQUESTED INSPECTIONS

ENG-81771
01/06/22

CONSTRUCTION NOTES:

19 PROTECT EXISTING ASPHALT RAISED CROSSING AND STRIPING.

70 INSTALL ACCESSIBLE PARKING SYMBOL PER DETAIL ON SHEET C-7.5.

71 INSTALL ACCESSIBLE PARKING ACCESS AISLE STRIPING PER DETAIL ON SHEET C-7.5.

72 INSTALL HIGH VISIBILITY CROSSWALK STRIPING PER DETAIL ON SHEET C-7.5.

73 INSTALL 4" WHITE, PAINTED PARKING STALL LINE PER DETAIL ON SHEET C7.5.

74 INSTALL 4" WHITE, PAINTED LANE LINE PER DETAIL ON SHEET C7.5.

75 INSTALL 4" YELLOW, PAINTED DOUBLE YELLOW CENTER LINE ON SHEET C7.5.

76 INSTALL PAINTED STOP BAR PER DETAIL ON SHEET C-7.5.

77 INSTALL WHITE, PAINTED TRAFFIC ARROW PER DETAILS ON SHEET C-7.5. SEE PLAN FOR TYPE AND APPROXIMATE LOCATIONS.

78 INSTALL STANDARD STOP SIGN PER DETAIL ON SHEET C-7.4.

79 INSTALL SINGLE SIDED ACCESSIBLE PARKING SIGN PER DETAIL ON SHEET C-7.4.

80 INSTALL DOUBLE SIDED ACCESSIBLE PARKING SIGN PER DETAIL ON SHEET C-7.4.

81 INSTALL 4" WHITE, PAINTED PEDESTRIAN CLEAR ZONE LINE.

82 INSTALL "RIGHT TURN ONLY" SIGN PER DETAIL ON SHEET C7.4.

83 INSTALL "WRONG WAY" SIGN PER DETAIL ON SHEET C7.4.

84 APPROXIMATE LOCATION OF FUTURE SCHOOL SIGN DONE BY OTHERS.

85 INSTALL PAINTED "ONLY" PER DETAIL ON SHEET C7.5.

86 INSTALL PAINTED RED CURB.

87 INSTALL PAINTED STENCILED WHAT "FIRE LANE NO PARKING" ON CURB.

88 REPLACE BICYCLE LANE MARKINGS PER CITY STANDARD DRAWING T29-43 ON SHEET C7.5.

PARKING COUNT

EXISTING STALLS TO REMAIN	31
NEW STANDARD STALLS	58
NEW COMPACT STALLS	7
NEW ACCESSABLE STALLS	5

BID SET

HARNEY ELEMENTARY SCHOOL
PARKING LOT EXPANSION
SIGNING AND STRIPING PLAN

Harper Houf Peterson Righellis Inc.
ENGINEERS • PLANNERS
LANDSCAPE ARCHITECTS • SURVEYORS
1220 Main Street, Suite 150, Vancouver, WA 98660
phone: 360.750.1131 www.hhpr.com fax: 360.750.1141

CHARLES L. HARPER, STATE OF WASHINGTON, REGISTERED PROFESSIONAL ENGINEER, 22293
12/15/2021

DESIGNED:	JWS/SJN
DRAWN:	JWS/SJN
CHECKED:	SJN/CLH
DATE:	12/15/2021

REVISIONS

DATE	NO.	DESCRIPTION

SHEET NO.
C6.0

JOB NO.
VPS-23

P:\02-Vancouver\VPS (Vancouver Public Schools)\VPS-23 (Harney Elementary Parking Expansion)\VPS23-DWGS\Sheets\C6 - SIGNING AND STRIPING PLAN.dwg